



# ROAD AND DRAINAGE LAYOUT OF PROPOSED RESIDENTIAL ESTATE

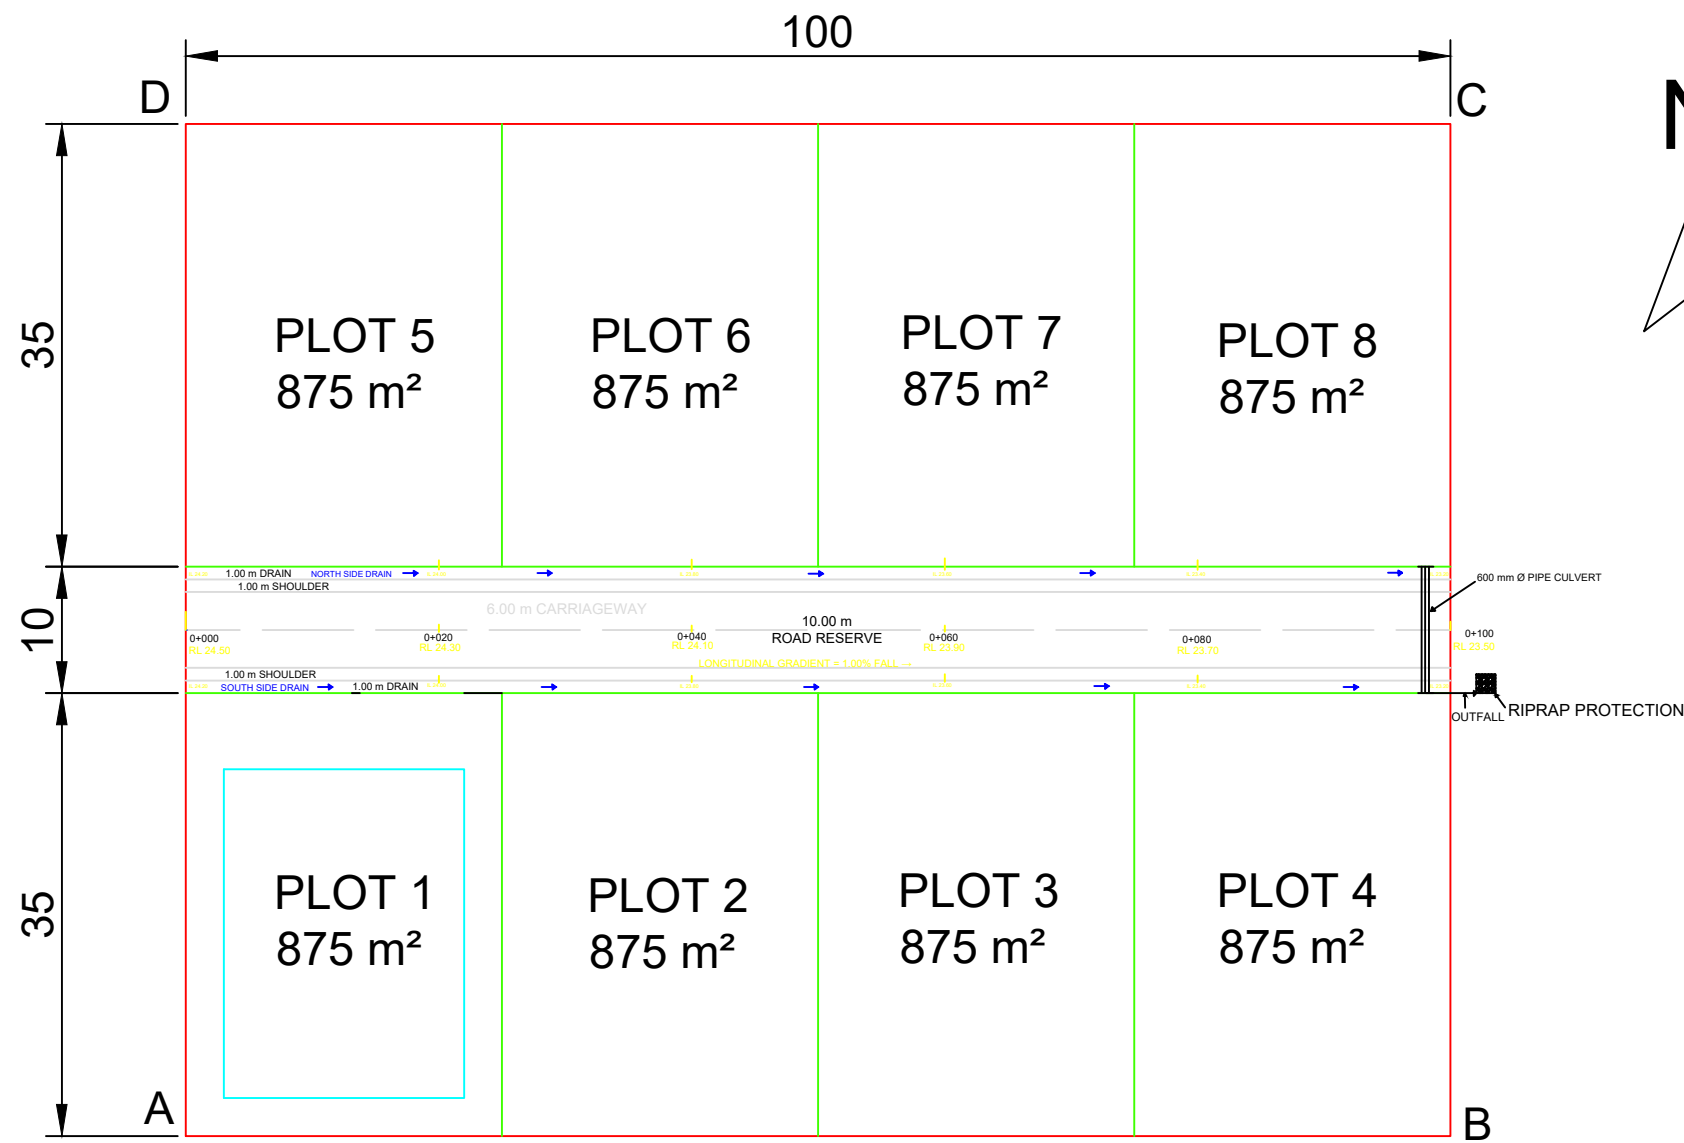

ROAD & DRAINAGE LEVEL SCHEDULE

| Chainage | Road RL (m) | Drain IL (m) |
|----------|-------------|--------------|
| 0+000    | 24.50       | 24.20        |
| 0+020    | 24.30       | 24.00        |
| 0+040    | 24.10       | 23.80        |
| 0+060    | 23.90       | 23.60        |
| 0+080    | 23.70       | 23.40        |
| 0+100    | 23.50       | 23.20        |

LEGEND

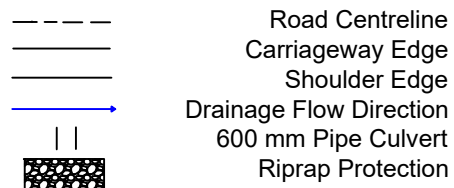

NOTES:

- All dimensions and levels are in metres unless otherwise stated.
- Road reserve width = 10.00 m.
- Carriageway width = 6.00 m.
- Shoulder width = 1.00 m on each side.
- Side drain width = 1.00 m on each side.
- Longitudinal road gradient = 1.00% fall toward Ch. 0+100.
- Drain invert levels are 0.30 m below road centreline levels.
- 600 mm pipe culvert and riprap protection are illustrative.
- Drawing prepared using simulated data for educational and portfolio purposes only.

PROJECT:  
Proposed Residential Estate

DRAWING:  
Road & Drainage Layout

DRAWN BY:  
Olaribigbe Olamiposi

SCALE:  
1:500

DATE:  
October 2026